


Picture	Name	Oty.	Power.	Weight.	Total Power	Total Weight.
	kinetic LED Pixel Line	72	220.0W	14.4 kg	15840 W	1036.8 kg
	kinetic LED Bar	36	120.0W	7.5kg	4320 W	270 kg

Total: 20.16 kW 1306.8 kg

Lighting Layout

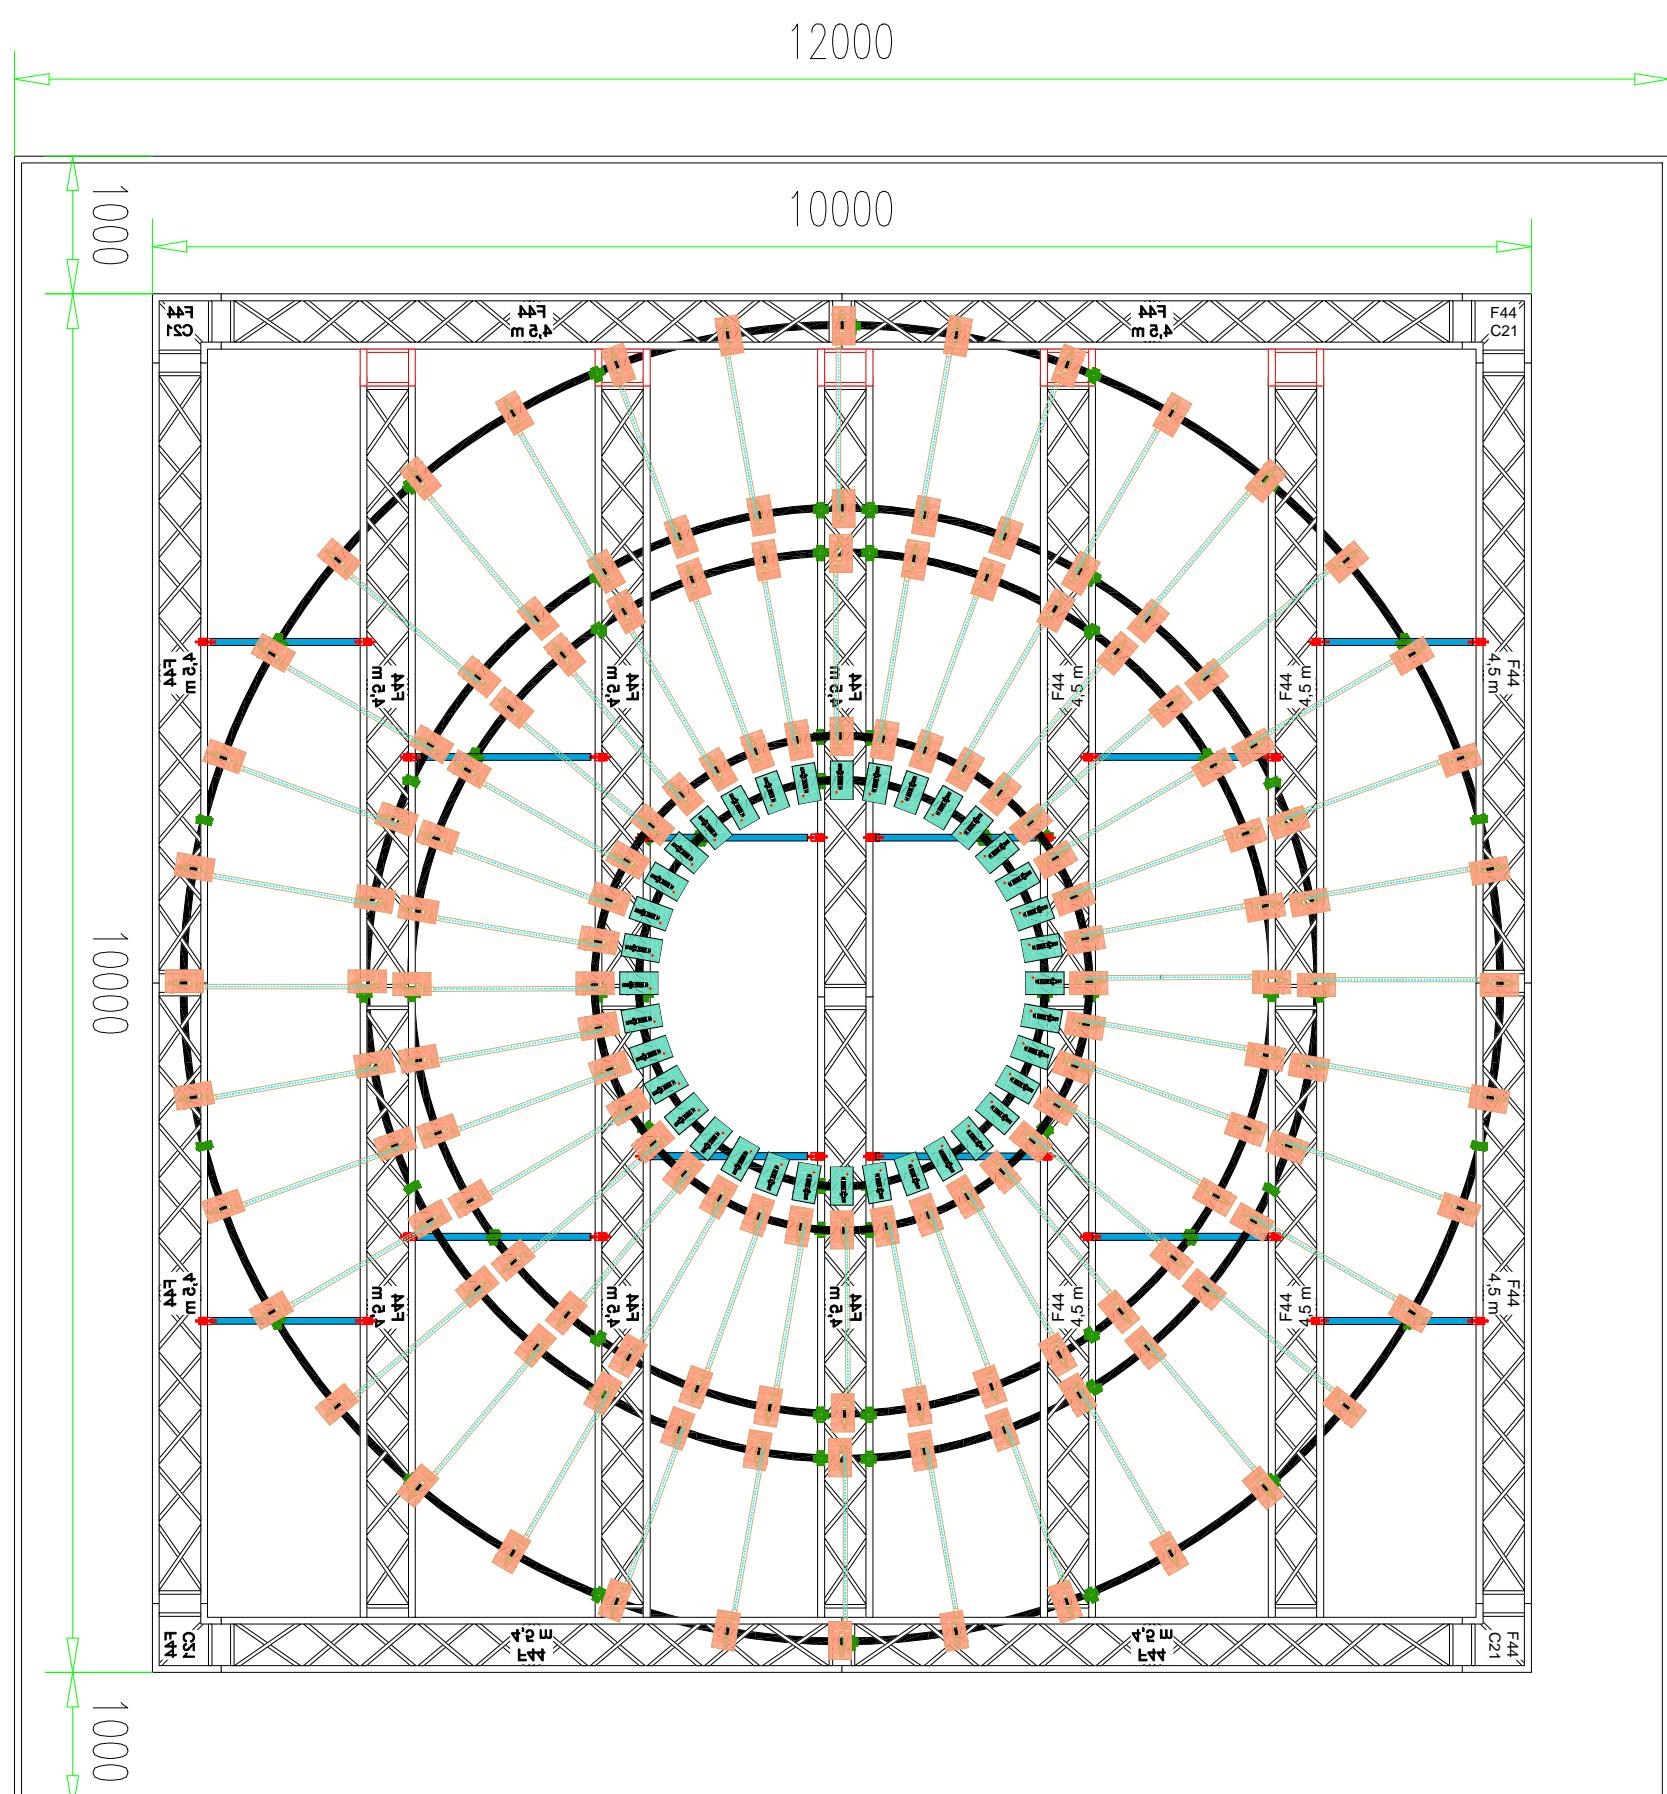

FENG-YI GROUP LIMITED
Leader of kinetic lights in China

CCTV partner
Global service capacity
Independent innovative products
Creative design team
Efficient customization service
Professional installation service

Address: No. 34, Fuyuan 1st Road,
Xinya Street, Huadu District,
Guangzhou, China
Phone: 0086-15018704285
Email: sales@fyilight.com
Website: www.fyilight.com

Project Name:
Monopol Berlin Plan

Drawing content:
Layout of kinetic lighting

Project Manager:
Lucy Gao

Designer:
Danilo Grande

Draftsman:
Jason Yang

Construction Manager:
Jimmy Zhang

Date:
2024.03.27

Version:
R3


The construction size is subject to
the marked size.
The construction unit must check
the size on site
If there is any discrepancy, please
notify the company immediately

Learn more video
<https://vimeo.com/user115756023>

This copyright belongs to FENG-YI GROUP LIMITED
It may not be reproduced, copied or disclosed without consent.

ALL RIGHTS RESERVED.

Truss Layout

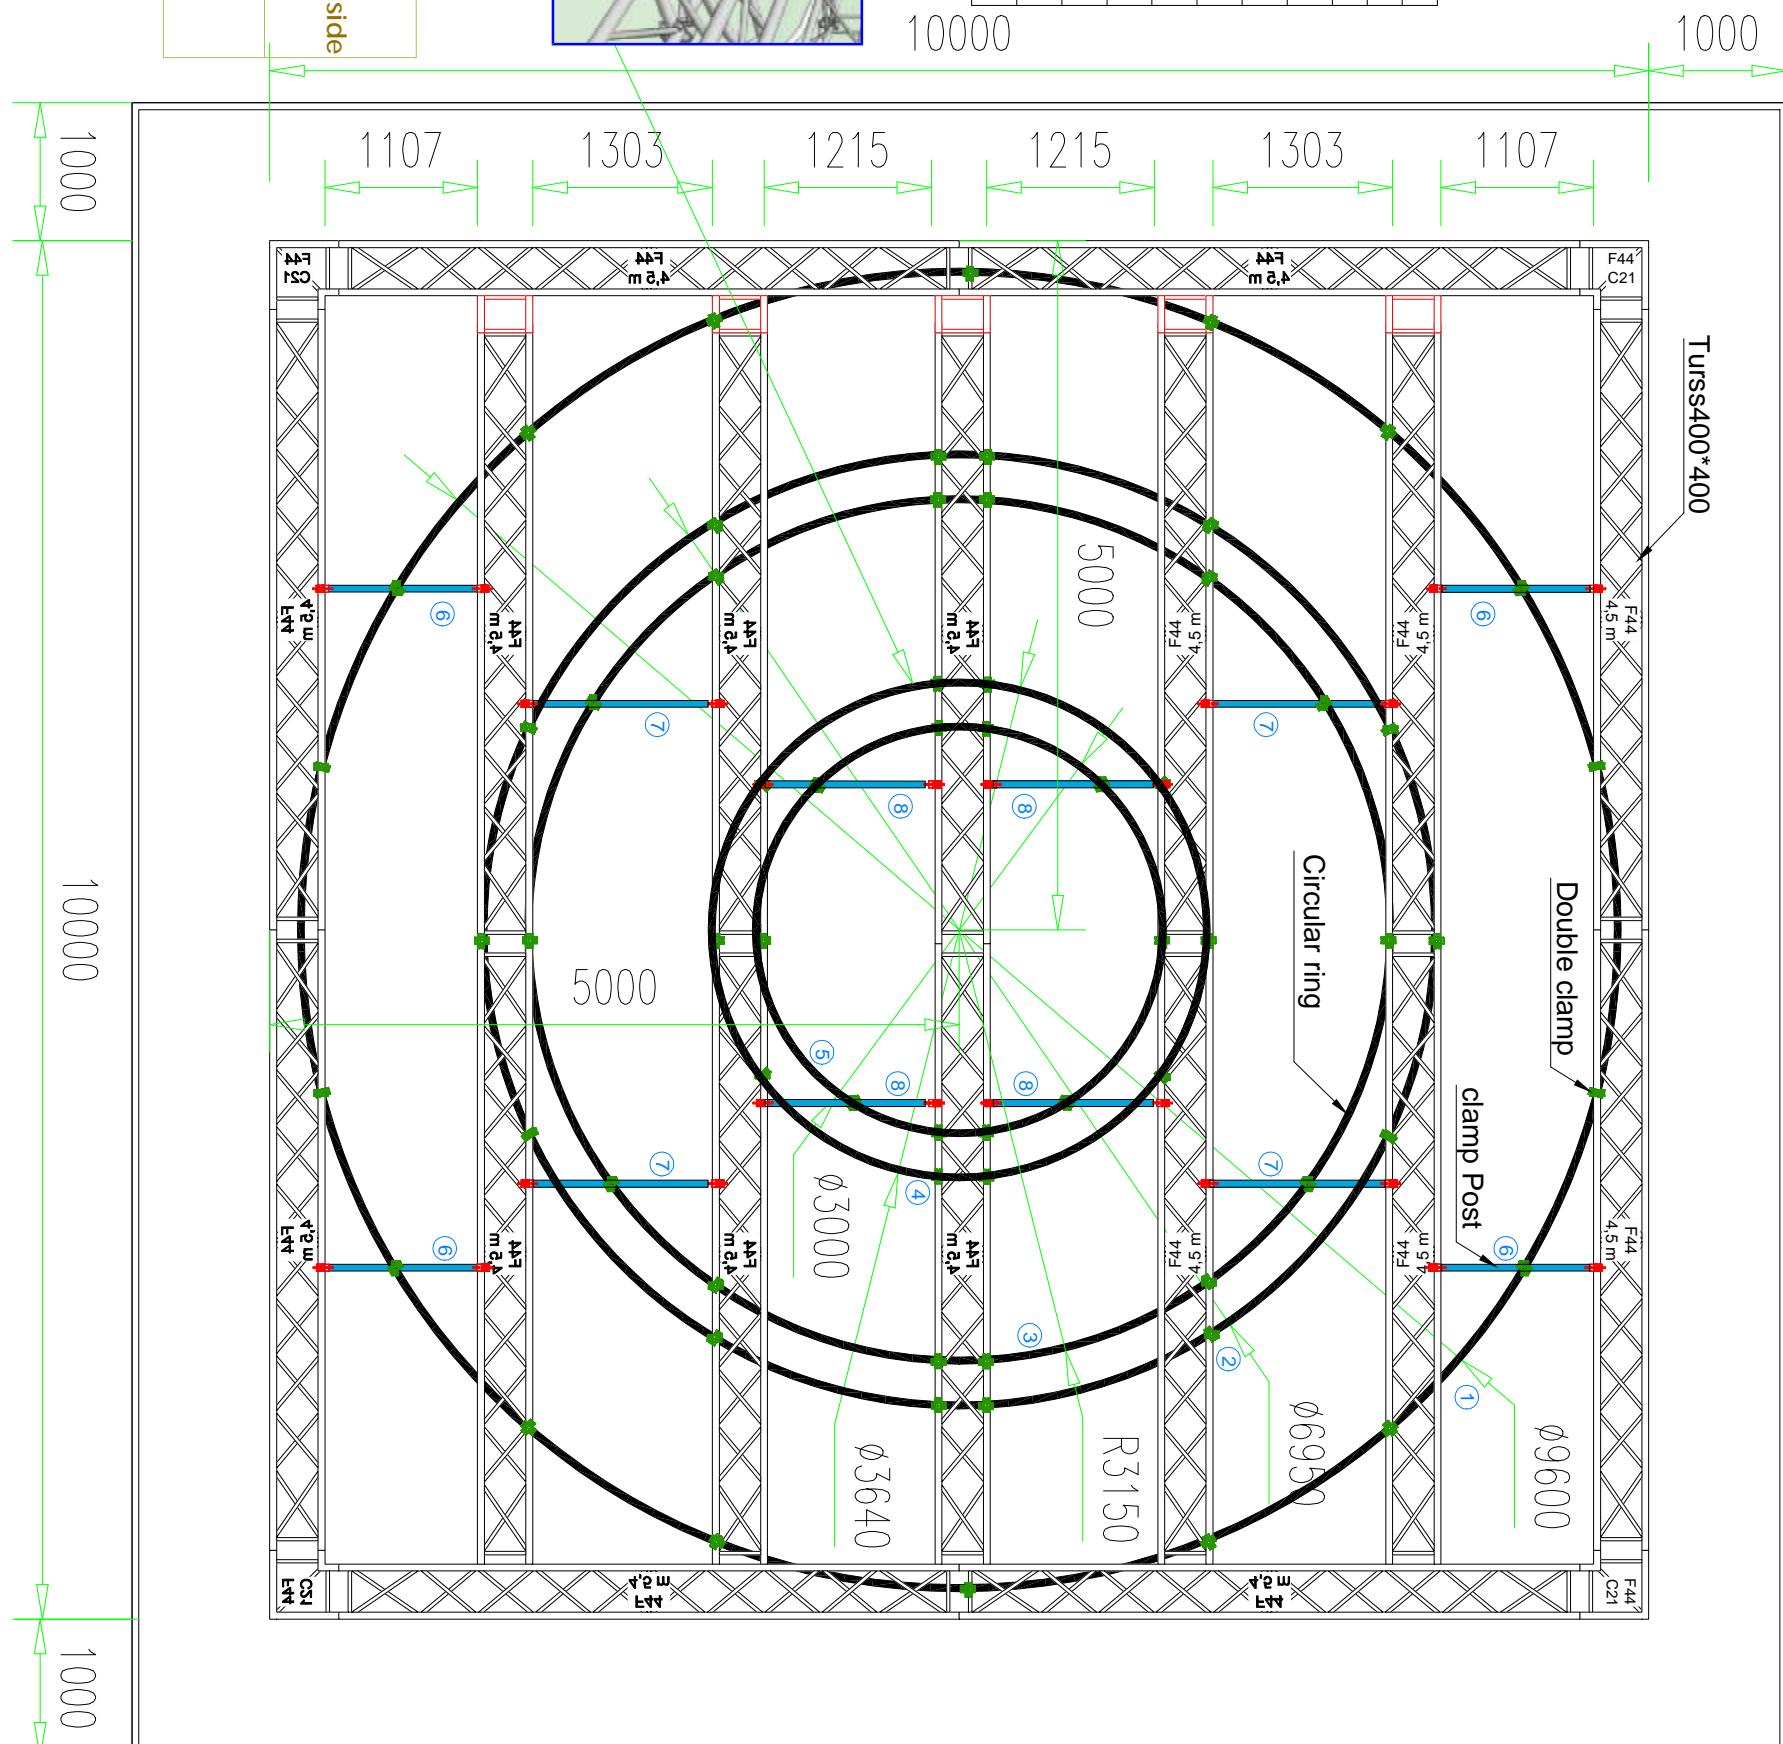

Circular ring connect with main truss under
 - 5 circular ring
Pipe+Single clamp connect with main truss side
 - 6 Pipe+Single clamp

Double clamp 66ps
 - 66Pcs for circular ring

Picture	Name	Qty.
	Double clamp	66
	Clamp	24
①	Circular ring of φ9600m*48mm*4mm	1
②	Circular ring of φ6960m*48mm*4mm	1
③	Circular ring of φ3640m*48mm*4mm	1
④	Circular ring of φ3150m*48mm*4mm	1
⑤	Circular ring of φ3000m*48mm*4mm	1
⑥	clamp Post of 1.11m * 48mm*4mm	4
⑦	clamp Post of 1.3m * 48mm*4mm	4
⑧	clamp Post of 1.22m * 48mm*4mm	4

FENG-YI GROUP LIMITED
Leader of kinetic lights in China
CCTV partner
Global service capacity
Independent innovative products
Creative design team
Efficient customization service
Professional installation service
FENG-YI D LB
This copyright belongs to FENG-YI GROUP LIMITED It may not be reproduced, copied or disclosed without consent.
ALL RIGHTS RESERVED.



Learn more video
<https://vimeo.com/user115756023>

Version: R3
 The construction size is subject to
 the marked size.
 The construction unit must check
 the size on site
 If there is any discrepancy, please
 notify the company immediately

Date: 2024.03.27
Construction Manager: Jimmy Zhang
Draftsman: Jason Yang
Designer: Lucy Gao



FENG-YI GROUP LIMITED
Leader of kinetic lights in China

CCTV partner
Global service capacity

Independent innovative products
Creative design team

Efficient customization service
Professional installation service

Address: No. 34, Fuyuan 1st Road,
Xing Street, Huidu District,
Guangzhou, China
Phone: 0086-15018704285
Email: sales@fyilight.com
Website: www.fyilight.com

Project Name:
Monopol Berlin Plan

Drawing content:
Power System 2

Project Manager:

Lucy Gao

Designer:
Danilo Grande

Draftsman:

Jason Yang

Construction Manager:
Jimmy Zhang

Date: **2024.03.27**


Version:

The construction size is subject to
the marked size.
The construction unit must check
the size on site
If there is any discrepancy, please
notify the company immediately.


Learn more videos
<https://vimeo.com/user115756023>

This copyright belongs to FENG-YI GROUP LIMITED
It may not be reproduced, copied or disclosed without consent.

Power system 2

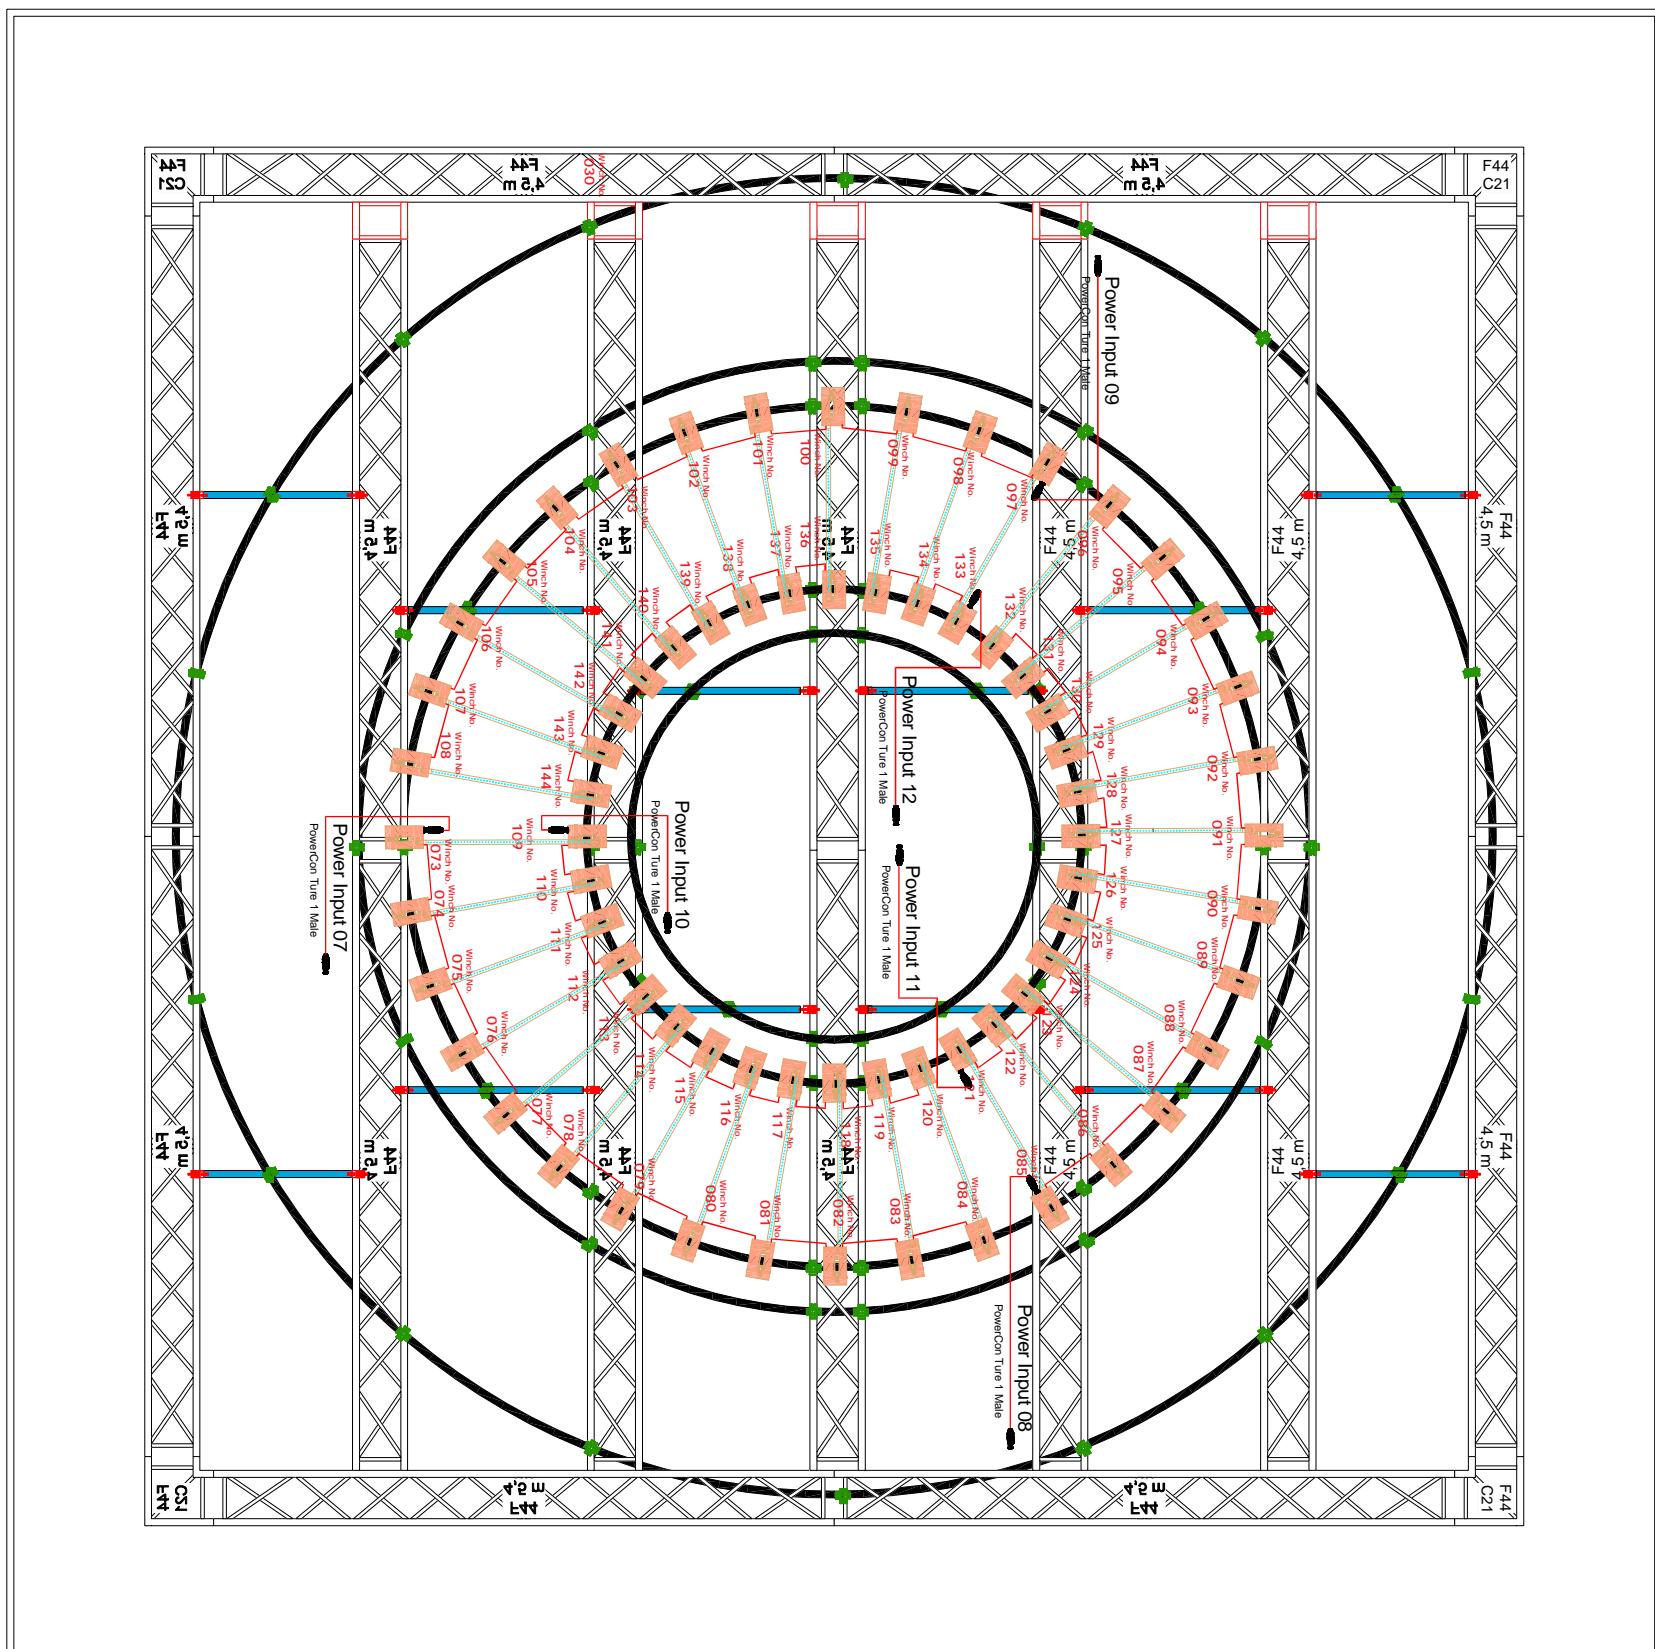

Power system

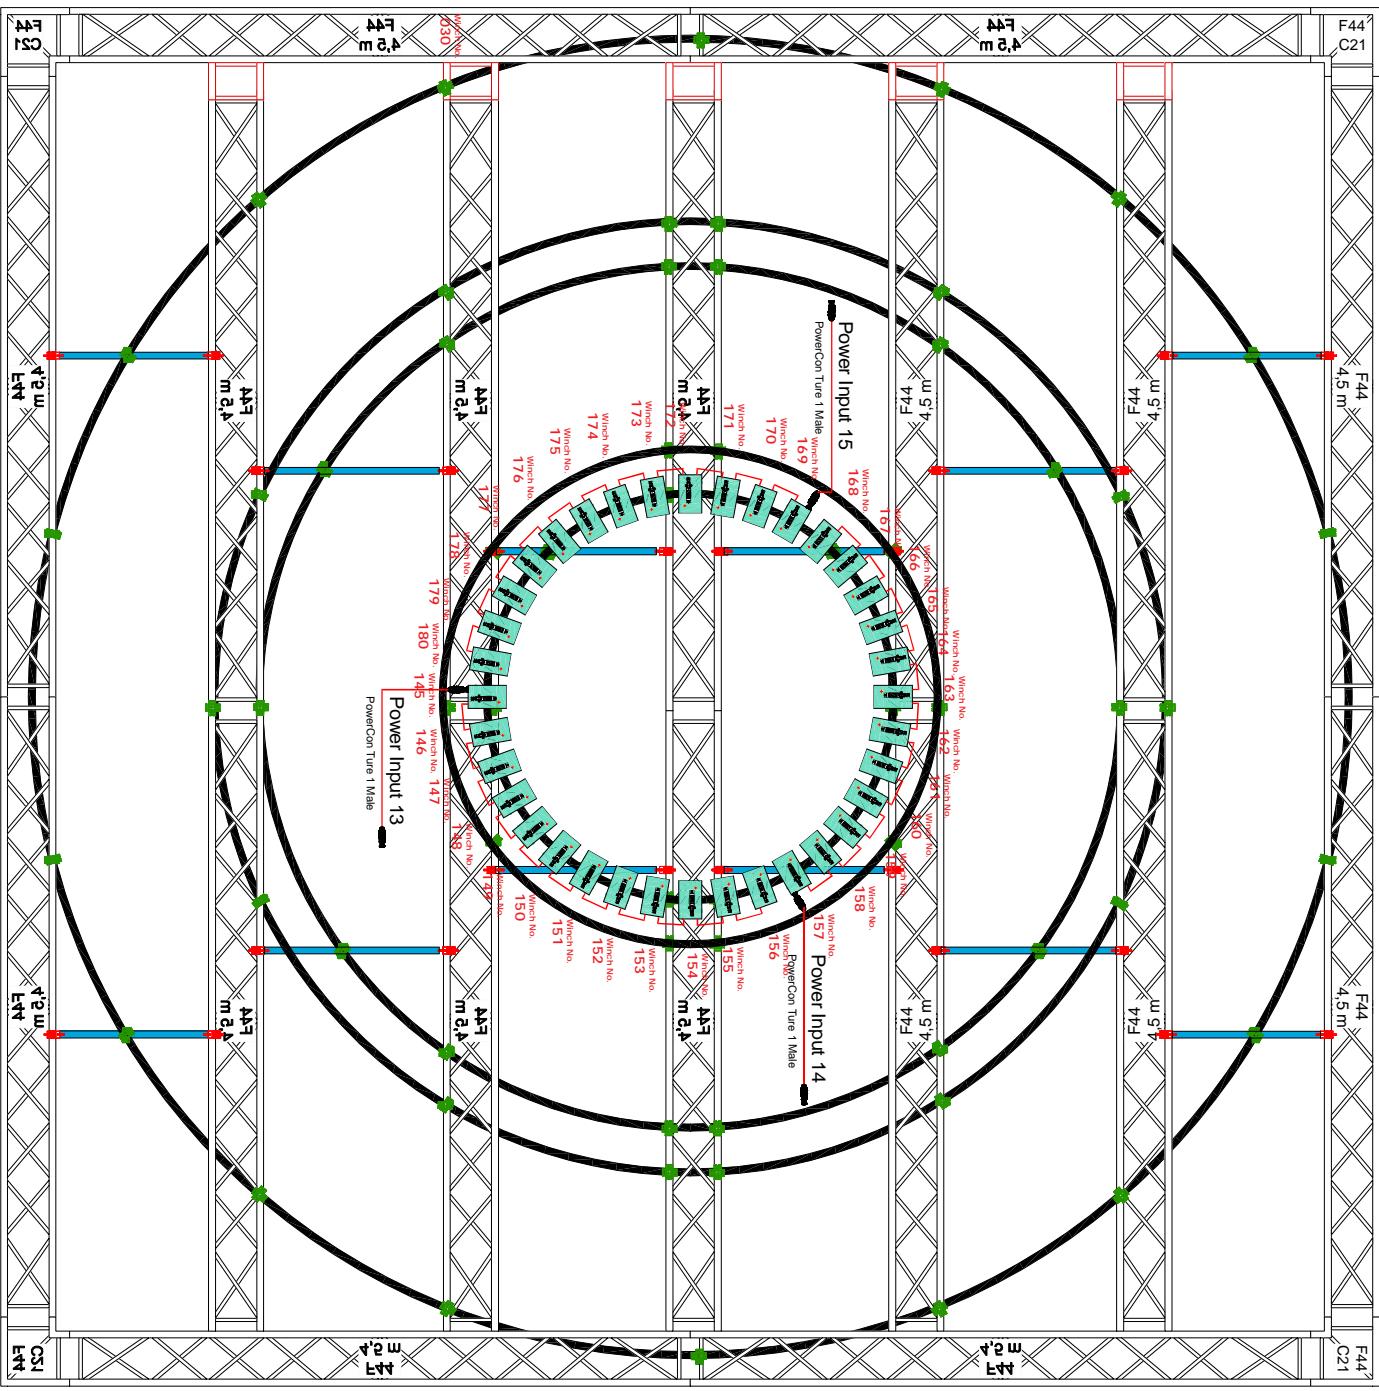

FENGYI GROUP LIMITED

Leader of kinetic lights in China
CCTV partner

Global service capacity

Creative design team
Independent Innovative products

Efficient customization service

Professional installation service

10 of 10

Address: No. 34, Fuyuan 1st Road
Xinya Street, Huadu District,
Guangzhou, China
Phone: 0086 15018704285

Email: sales@fylight.com
Website: www.fylight.com

Project Name: _____

Molecular Biology

Drawing content:

Project Manager:

Lucy Gao

Designer:

Danilo Grande

Draftsman:

Jason Yang

Construction Manager:

July 2014

Date: 2024.03.27

Version:

卷之三


The construction size is subject to the marked size
The construction unit must check the size on site
If there is any discrepancy, please notify the company immediately

[Learn more videos](https://vimeo.com/user115756023)

<https://vimeo.com/user115756023>

This copyright belongs to FENGYI GROUP LIMITED.
It may not be reproduced, copied or disclosed without consent.

Contron system

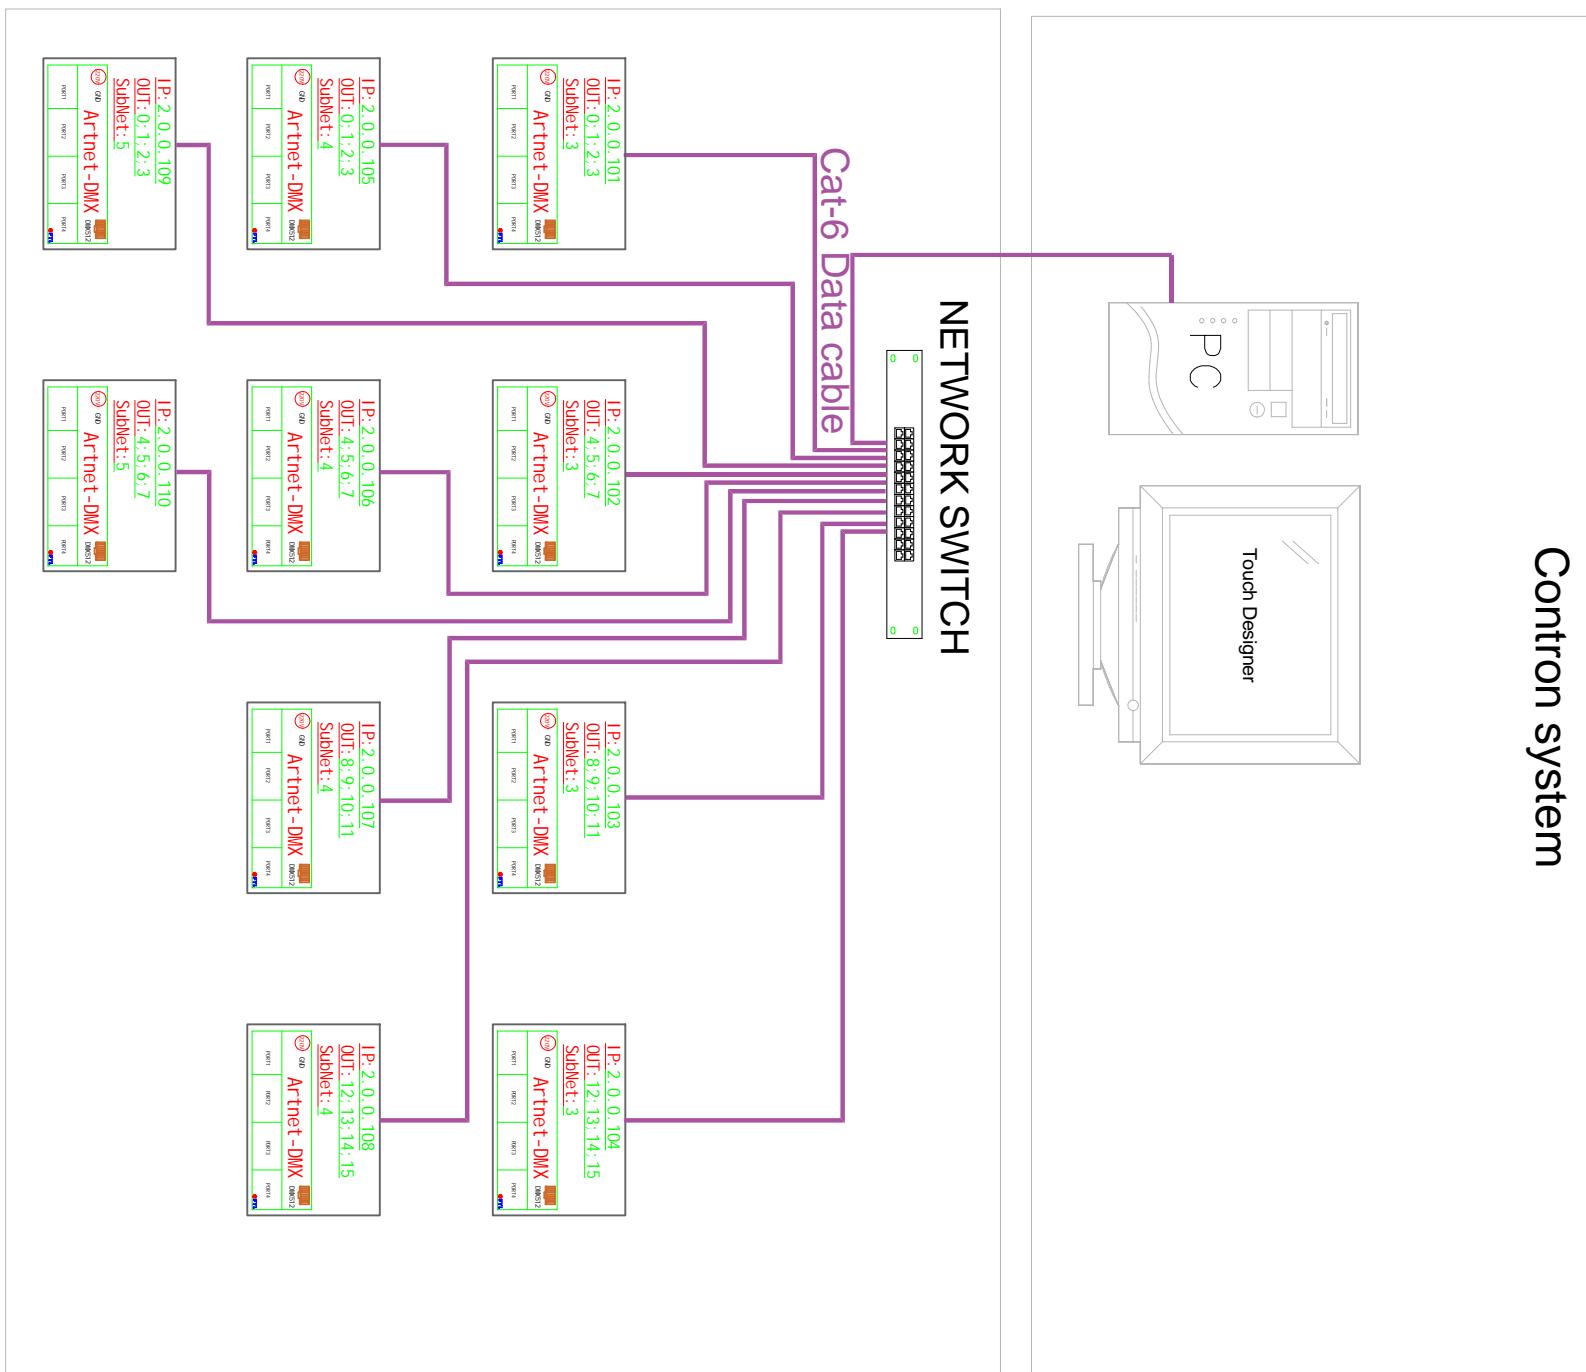

Project Name:	Monopol Berlin Plan
Drawing content:	Signal system
Project Manager:	Lucy Gao
Designer:	Danilo Grande
Draftsman:	Jason Yang
Construction Manager:	Jimmy Zhang

Address: No. 34, Fuyuan 1st Road,
Xinya Street, Huangpu District,
Guangzhou, China
Phone: 0086-15018704285
Email: sales@fyilight.com
Website: www.fyilight.com



This copyright belongs to FENG-YI GROUP LIMITED.
It may not be reproduced, copied or disclosed without consent.

Learn more videos
<https://vimeo.com/user115756023>

ALL RIGHTS RESERVED.



FENG-YI GROUP LIMITED
Leader of kinetic lights in China

CCTV partner
Global service capacity

Independent innovative products
Creative design team
Efficient customization service
Professional installation service

Address: No. 34, Fuyuan 1st Road,
Xingye Street, Haadu District,
Guangzhou, China
Phone: 0086-15018704285
Email: sales@fyilight.com
Website: www.fyilight.com

Drawing content:
Signal system 1
Project Name: **Monopol Berlin Plan**

Project Manager: **Lucy Gao**
Designer: **Danilo Grande**

Draftsman: **Jason Yang**
Construction Manager: **Jimmy Zhang**


Date: **2024.03.27**
Version:

The construction size is subject to
the marked size.
The construction unit must check
the size on site
if there is any discrepancy, please
notify the company immediately.

Learn more video
<https://vimeo.com/user115756023>

This copyright belongs to FENG-YI GROUP LIMITED
It may not be reproduced, copied or disclosed without consent.

Signal system 1

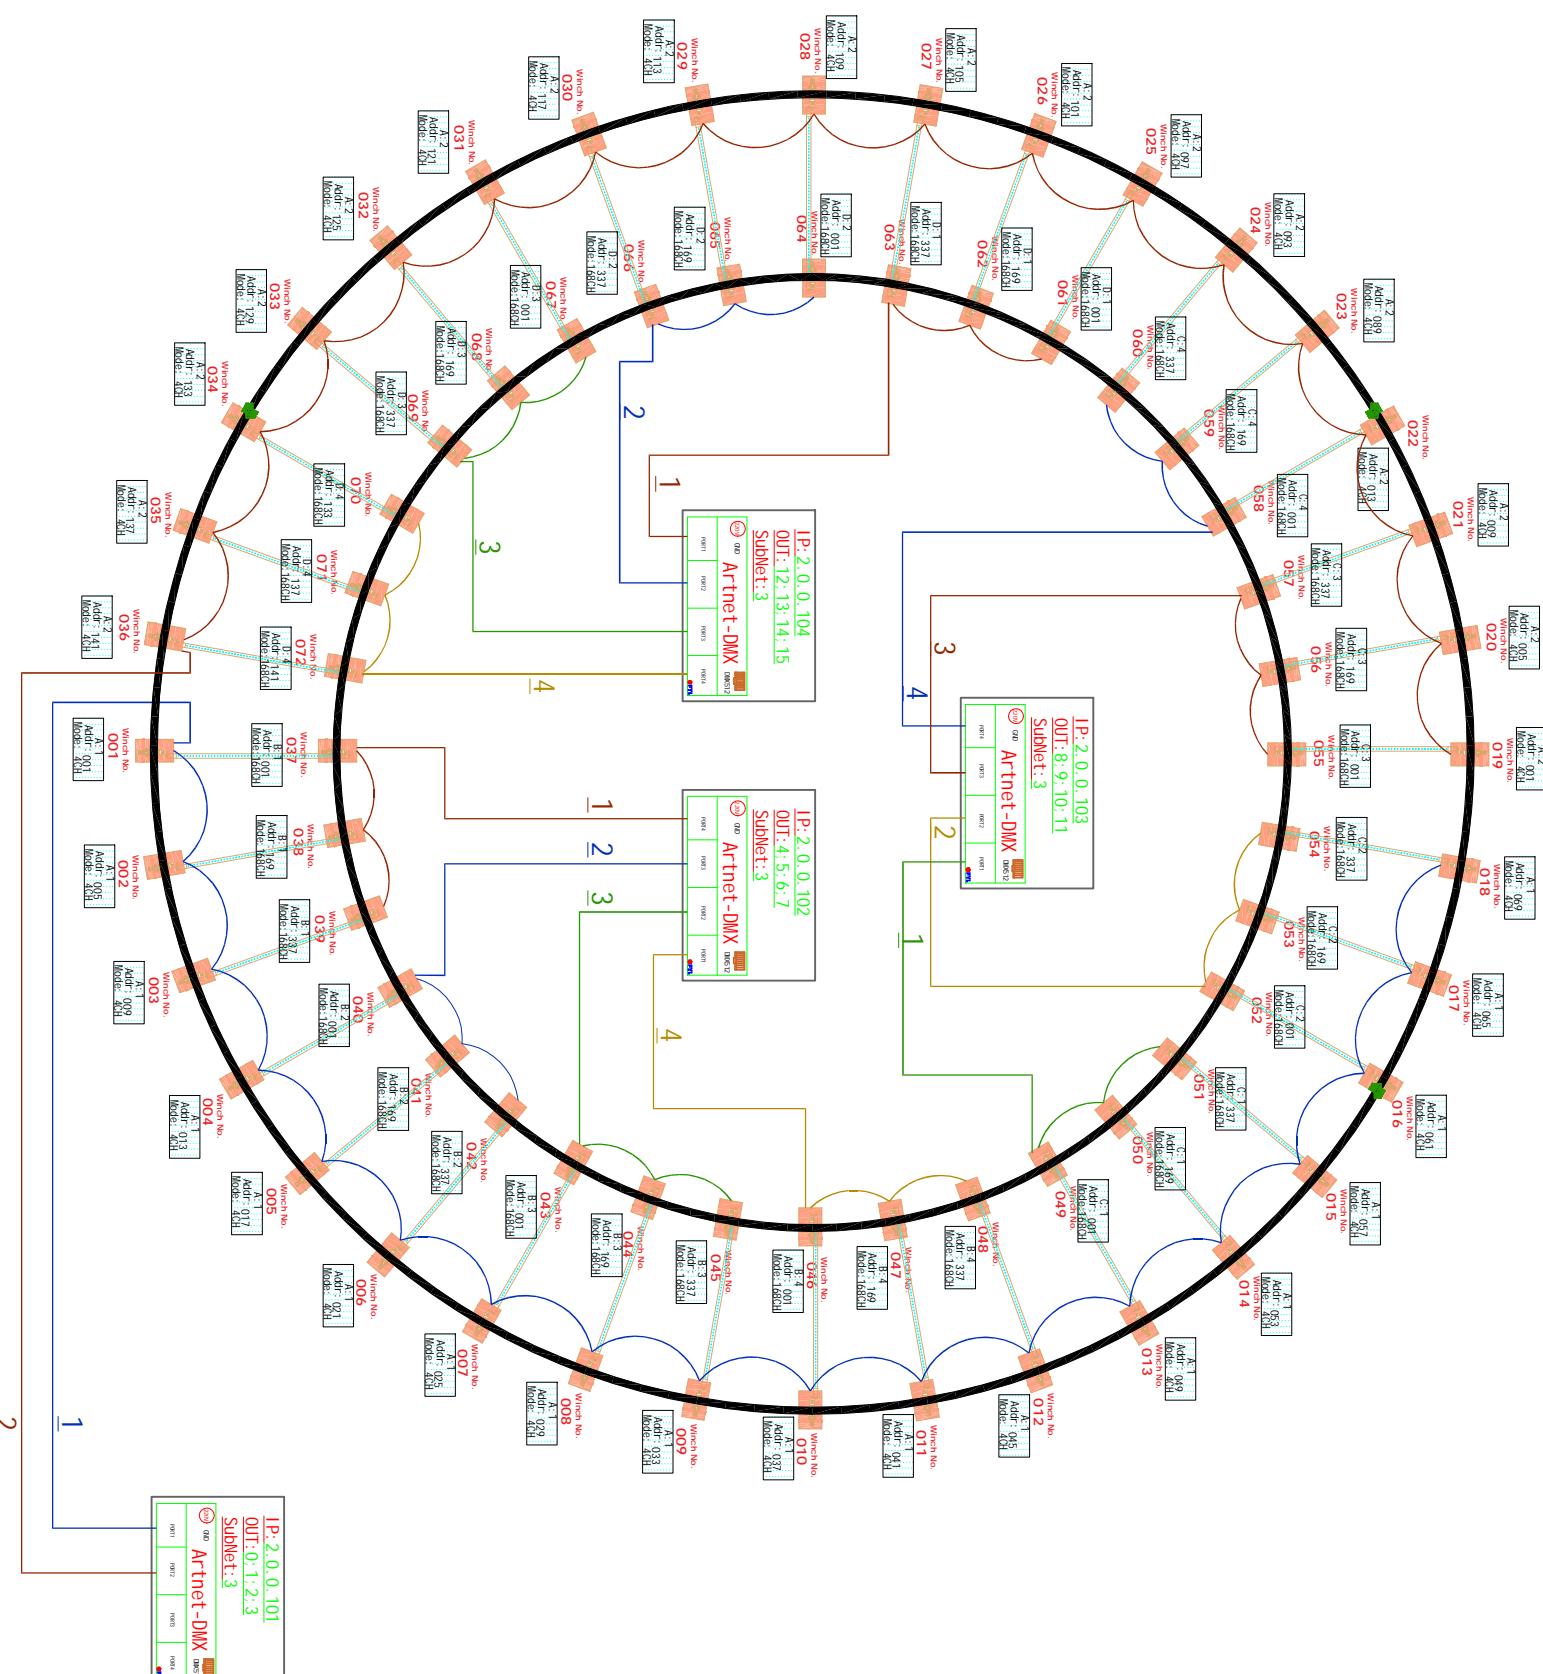



FENG-YI GROUP LIMITED

Leader of kinetic lights in China
CCTV partner
Global service capacity
Independent innovative products
Creative design team
Efficient customization service

Address: No. 34, Fuyuan 1st Road,
Xing Street, Haadu District,
Guangzhou, China
Phone: 0086-15018704285
Email: sales@fyilight.com
Website: www.fyilight.com

Project Name:

Signal system 1

Drawing content:
Control signal system diagram

Project Manager:
Lucy Gao


Designer:
Danilo Grande

Draftsman:
Jason Yang

Construction Manager:
Jimmy Zhang

Date: **2024.03.27**

Version:

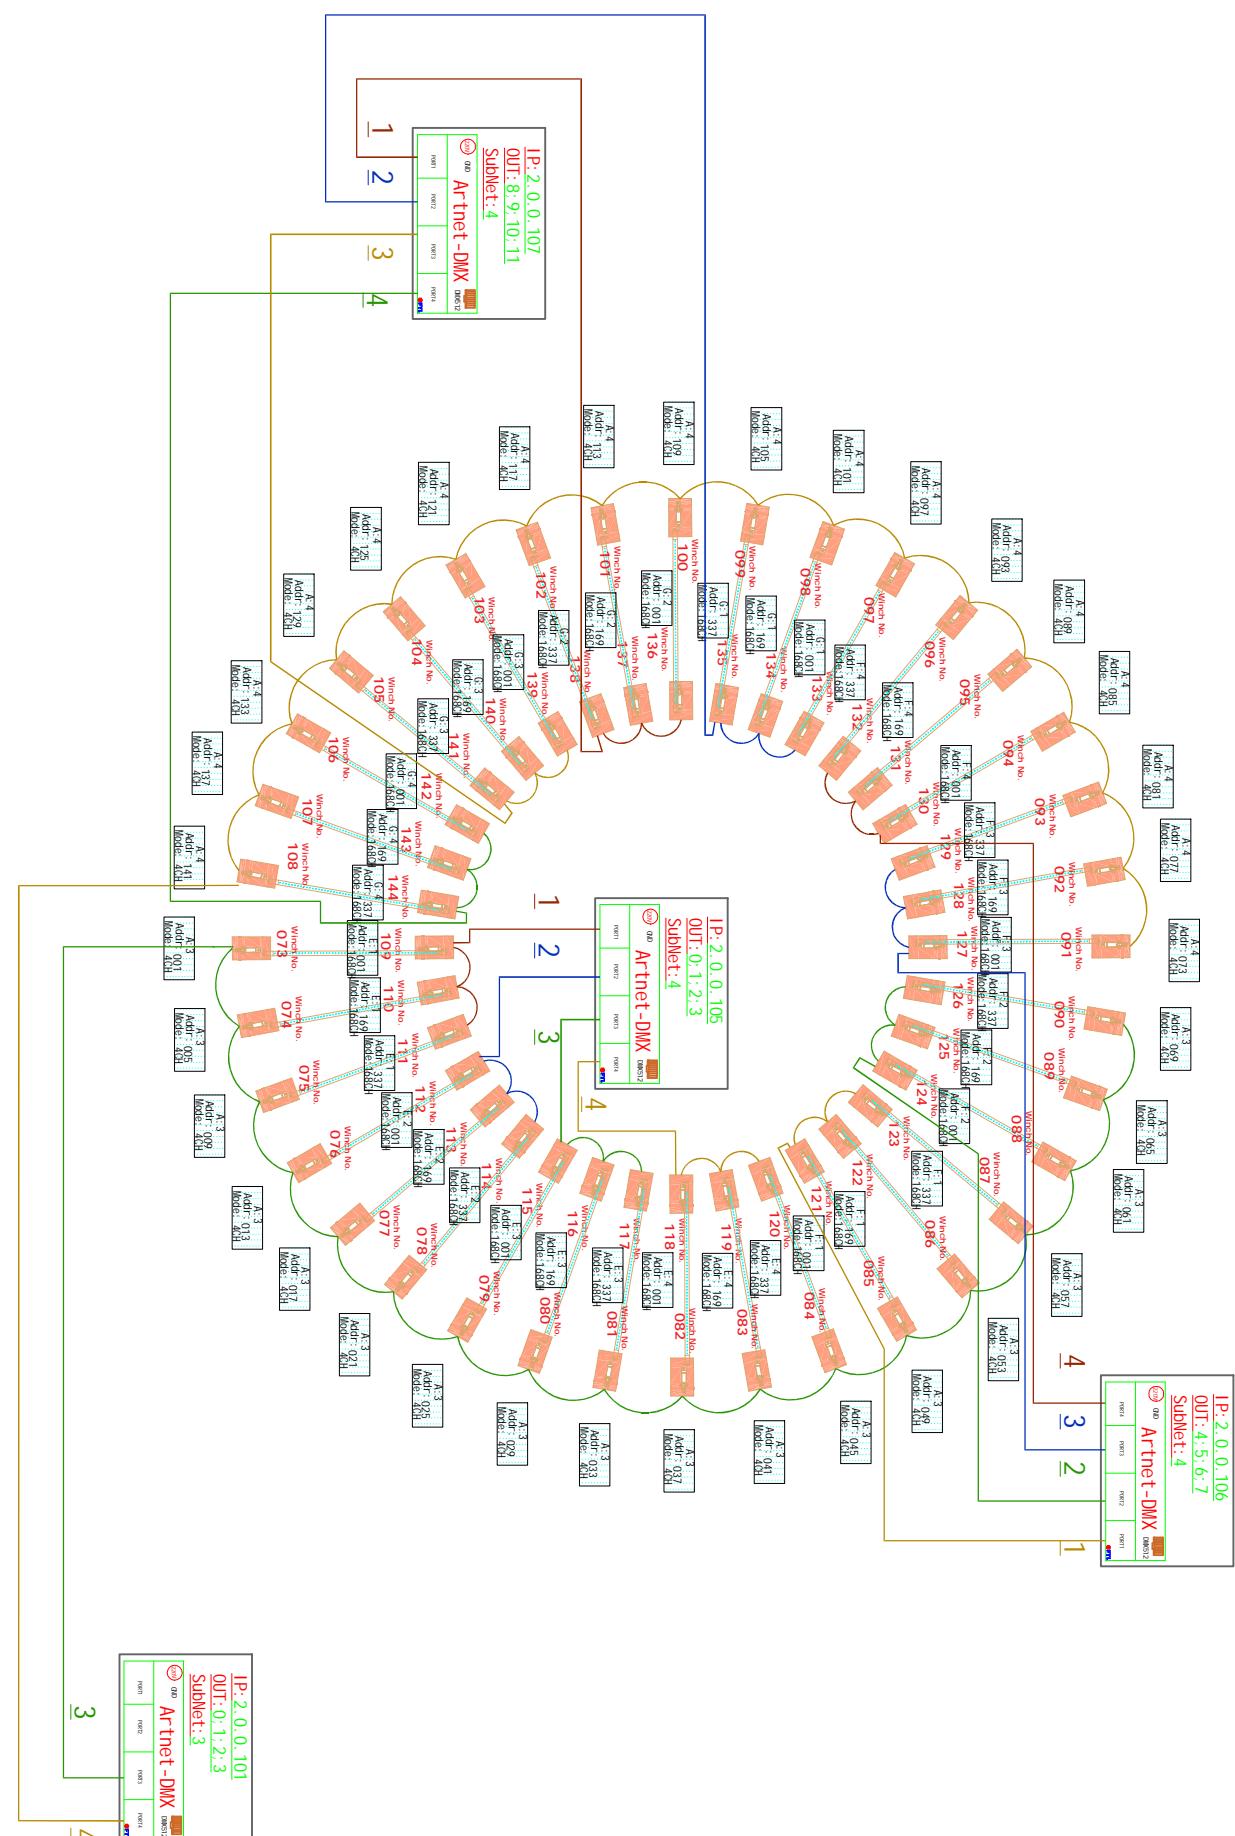

Signal system


Learn more videos
<https://vimeo.com/user115756023>

The construction size is subject to
the marked size.
The construction unit must check
the size on site
If there is any discrepancy, please
notify the company immediately

This copyright belongs to FENG-YI GROUP LIMITED
It may not be reproduced, copied or disclosed without consent.

ALL RIGHTS RESERVED.

Signal system

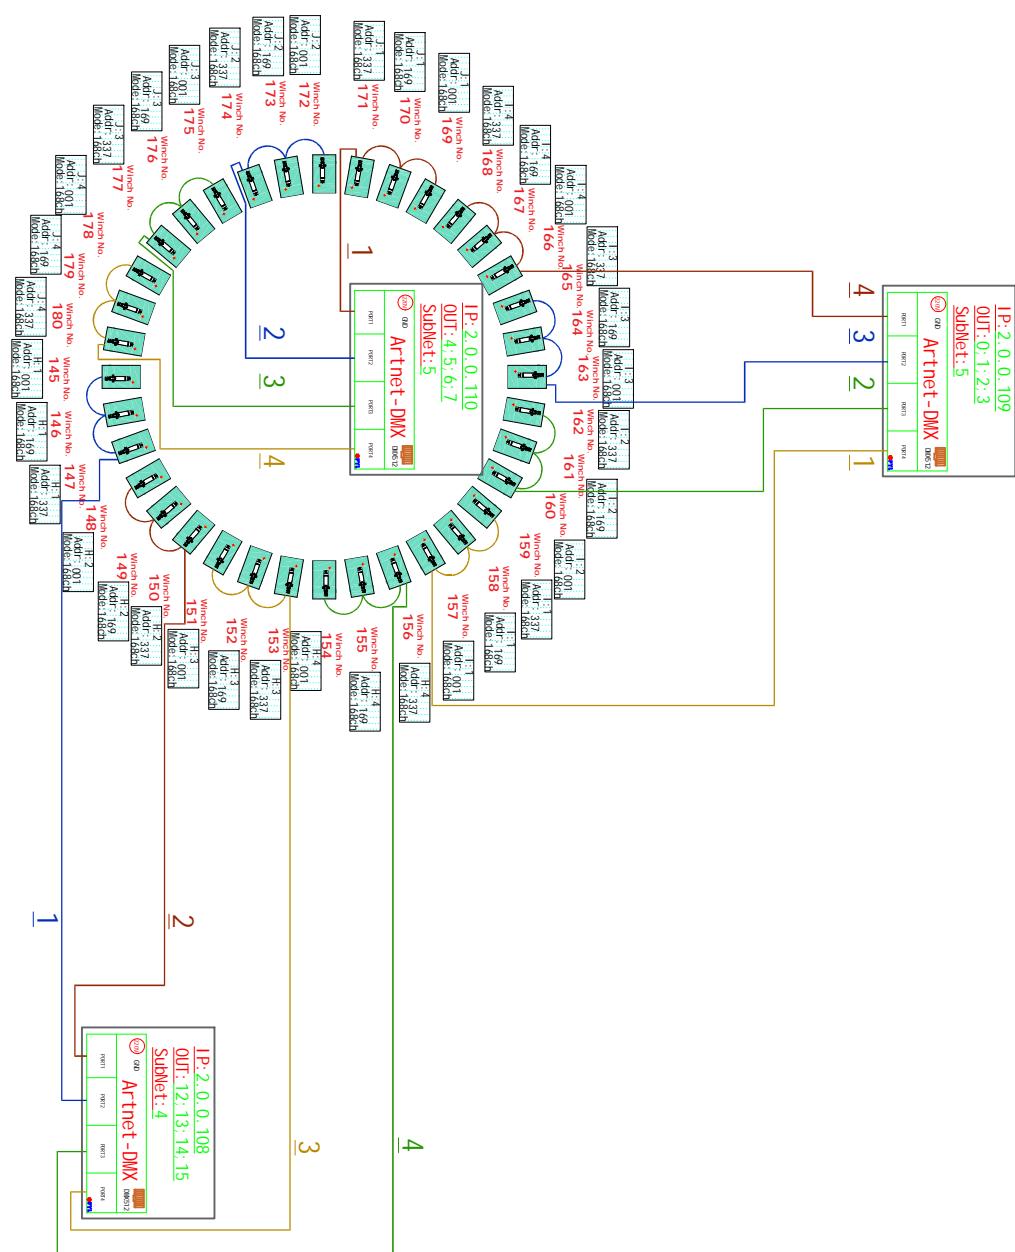

FENGYI GROUP LIMITED
Leader of kinetic lights in China
CCTV partner

Global service capacity
Independent innovative products
Creative design team
Efficient customization service
Professional installation service

Address: No. 34, Fuyuan 1st Road,
Xingya Street, Haadu District,
Guangzhou, China

Phone: 0086-15018704285

Email: sales@fyilight.com

Website: www.fyilight.com

Project Name:
Monopol Berlin Plan

Drawing content:
Signal system 1

Project Manager:
Danilo Grande

Designer:
Lucy Gao

Draftsman:
Jason Yang

Construction Manager:
Jimmy Zhang

The construction size is subject to
the marked size.
The construction unit must check
the size on site
If there is any discrepancy, please
notify the company immediately

Learn more videos
<https://vimeo.com/user115756023>

This copyright belongs to FENGYI GROUP LIMITED
It may not be reproduced, copied or disclosed without consent.

ALL RIGHTS RESERVED.